Architecture 6: Structural 3-Level 4:2 CSA Wallace Reduction Tree
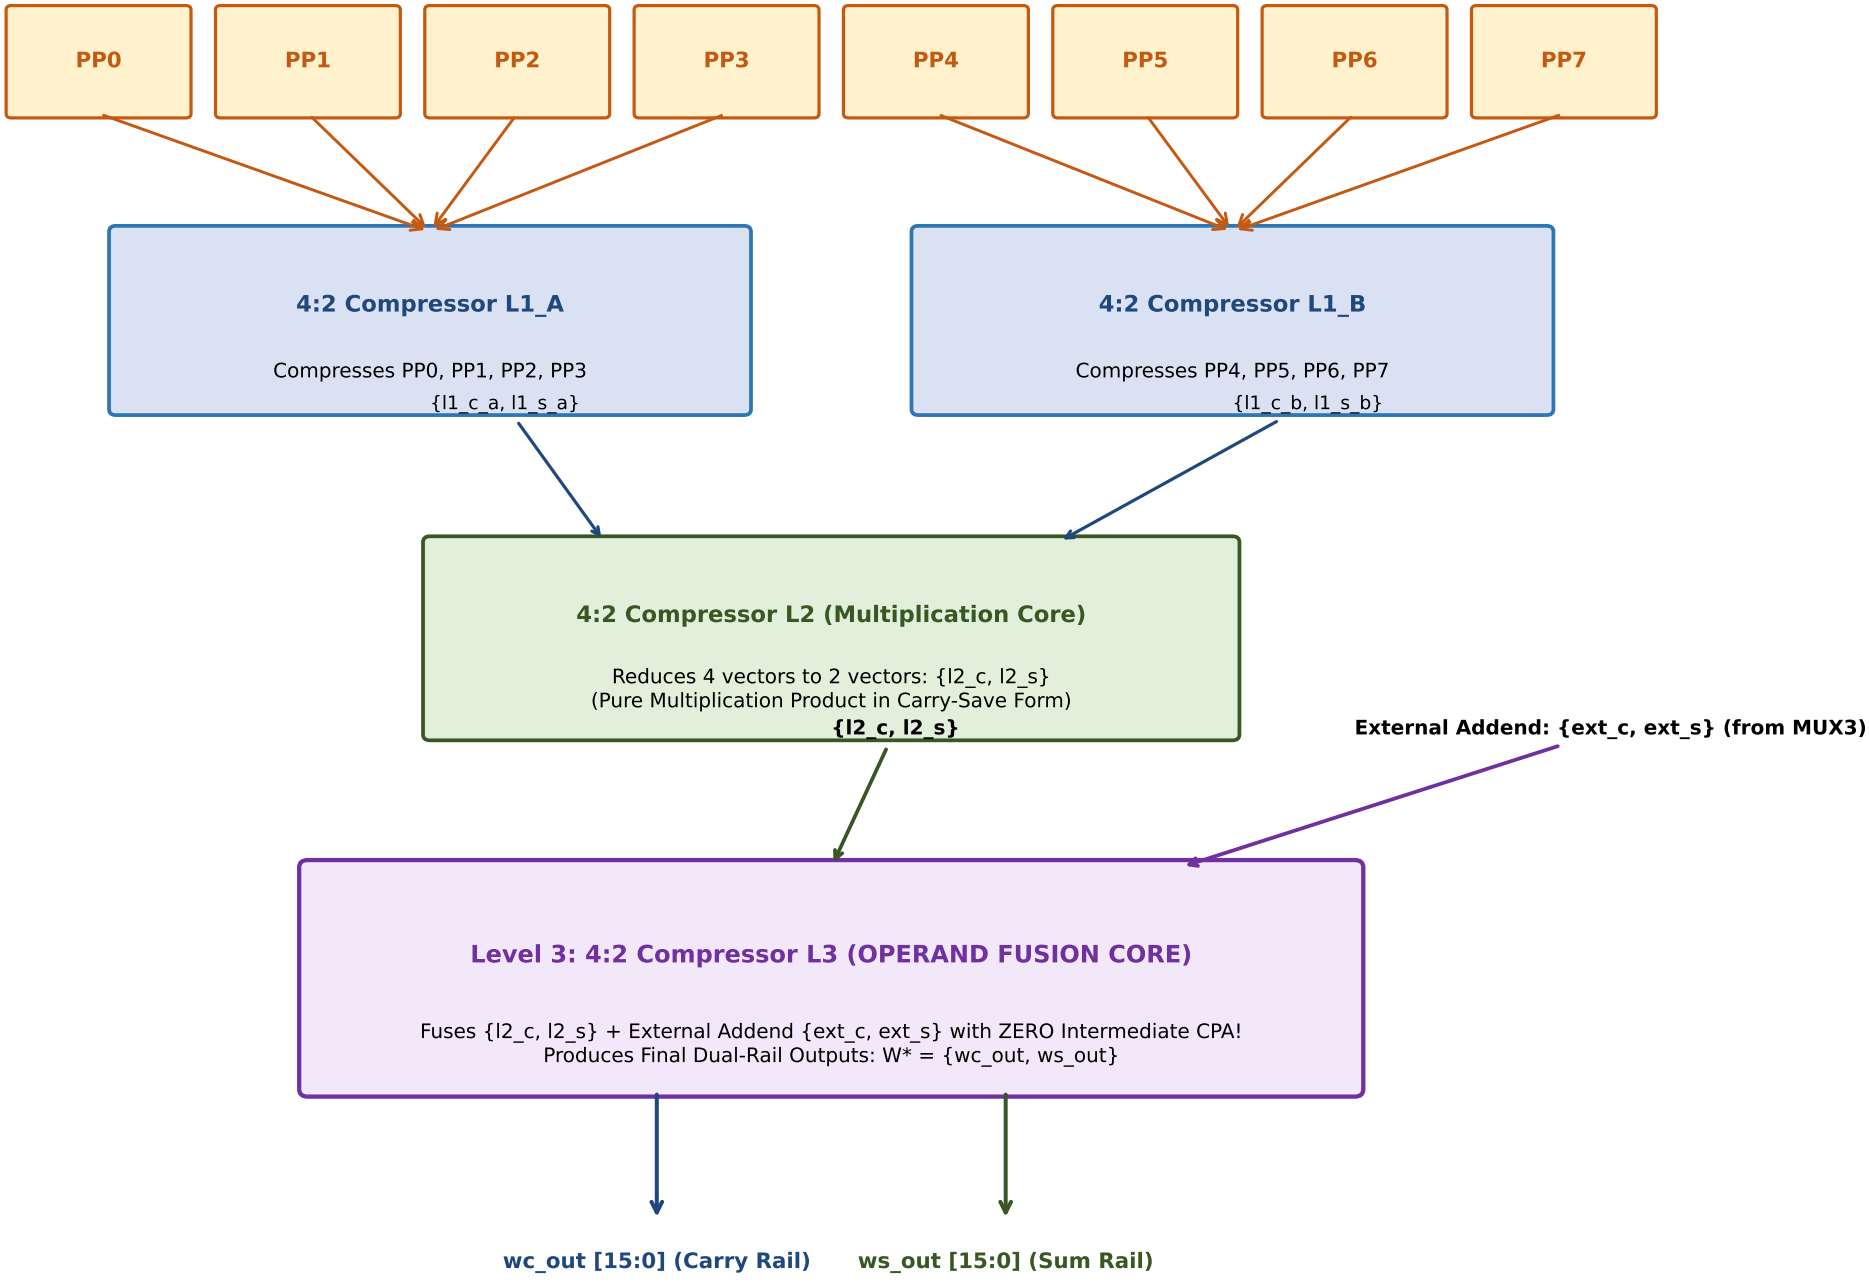
Compresses 8 Booth Partial Products + Directly Fuses Dual-Rail External Addend with Zero CPA